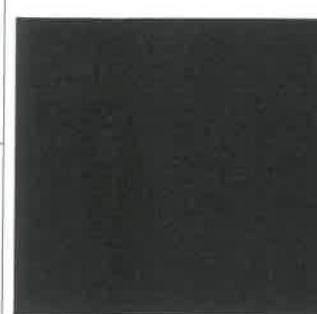


C&W DESIGN + BUILD		
Debevoise & Plimpton		
OF-AEE-21-90550 DEBEVOISE_PROJECT		
NOTE: All designs are the sole property of C&W Design + Build and may not be used without their written permission. Exposed dimensions only are to be used for the manufacture of joinery. Any deviation from the design or the Supply of materials or any other part of the project will be at the client's risk. The Supplier shall bear full responsibility for any damage caused by any such deviation or fault.		
PHASE DESIGN		
DOCUMENT	APPROVALS	CLIENT
50.01 Joinery references plan, level +4	C&W D+B	
Print date: 21/01/22 Scale: 1:100		
REVISION		
D1	ID	Non de changement
D2		16/10/21
D3		21/10/21
D4		25/11/21
D5		1/12/21
D6		9/12/21
D7		14/12/21
E1		21/01/22

Code M 102	VYNIL		Code M 103	YOSEMITE		Code M 200	Stratifié	
Brand Model Colour Finish Size_L Size_W Size_H Diam	INTERFACE Textured Stones A00304 Emperador Gray	Sample / Image 	Brand Model Colour Finish Size_L Size_W Size_H Diam	YOSEMITE BLUSTYLE ROCK LAPPATA	Sample / Image 	Brand Model Colour Finish Size_L Size_W Size_H Diam	FENIX Fenix NTM 0720 Nero Ingo	Sample / Image 
Comment			Comment	BLUESTYLE ROCK LAPPATA		Comment		

C&W DESIGN + BUILD

CLIENT

Debevoise & Plimpton

PROJECT
OF-ABE-21.90550

DEBEVOISE_PROJECT

#Adresse complète du Site

Code M 201	LAMINATE		Code M 202	LAMINATE	
Brand Model Colour Finish Size_L Size_W Size_H Diam	EGGER White Levanto Marble	Sample / Image 	Brand Model Colour Finish Size_L Size_W Size_H Diam	EGGER Natural Carini Walnut	Sample / Image 
Comment			Comment		

NOTE
All designs are the sole property of Cushman&Wakefield Design+Build and may not be used without their written permission. Figured dimensions only are to be used 'For Construction' and any scaling of the drawing will be at the Supplier's risk. Suppliers are to verify all dimensions on-site and any discrepancies shall be addressed in writing to this office for clarification prior to the commencement of the work, otherwise the Supplier shall bear full responsibility for any associated cost. Any claims for variations or extras shall be submitted to this office for assessment prior to approval of any such variation or extra.

ISSUE

DESIGN

Print Date: 21/01/22 - 17:29 / ALU-21.90550 (DEBEVOISE)
Last save: Dernier enregistrement par

ID
100
MATERIAL SCHEDULE
100.05
Material Schedule

Original scale : 1:1
Drawing scale : 1:1,00
Print date : 21/01/22
Issued by : #Dernier enregistrement par
Approved by : YYYY

REVISION

E1


DOCUMENT N°

100.05

PAGE :

Page : 24/24


COMMANDER
ÉCHANTILLONS ✓

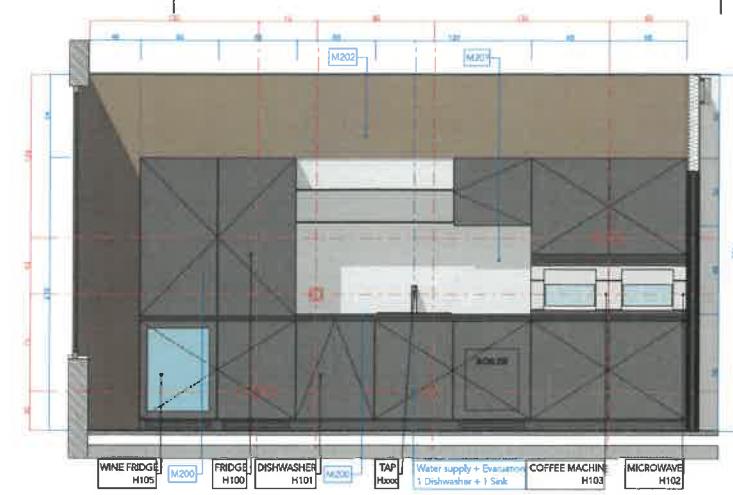


A.1 KITCHEN 1:20



A.2 KITCHEN 1:20

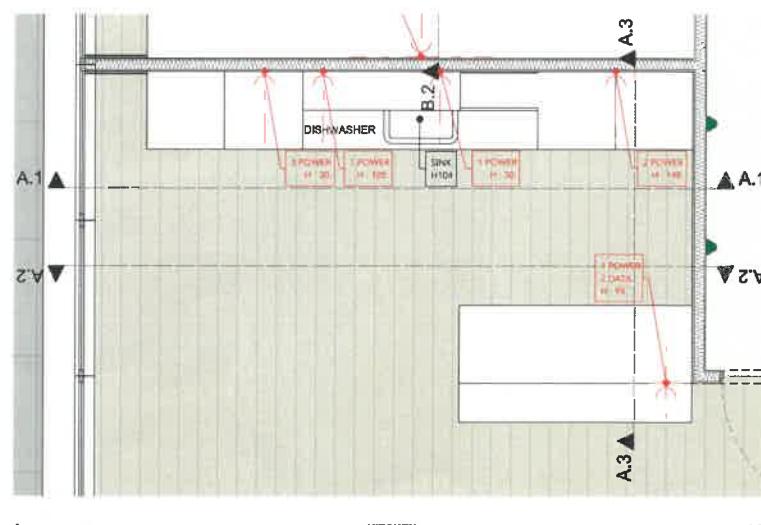


A. KITCHEN 1:20

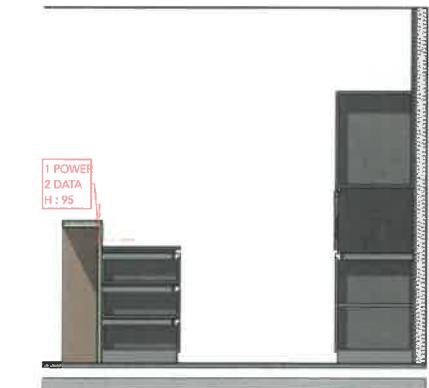

A.3 KITCHEN 1:20




KITCHEN Perspective 1:94.27

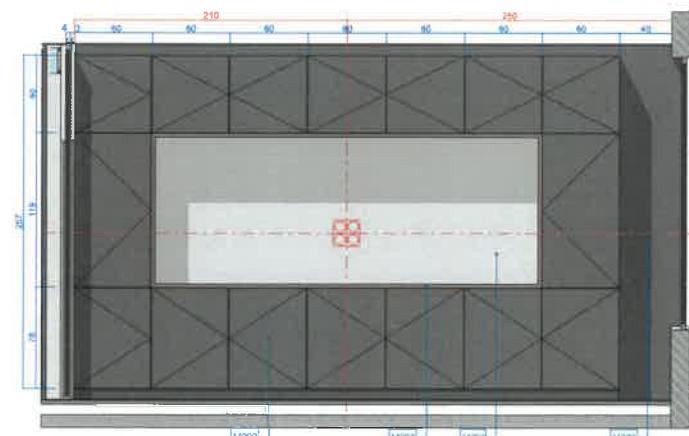


B.1 MEETING ROOM Cupboard 1:20




B.2 MEETING ROOM Cupboard 1:20

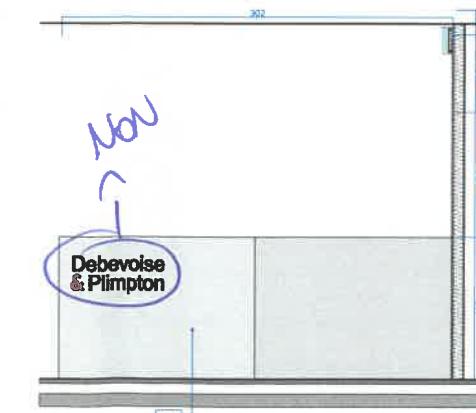



C.1 RECEPTION DESK 1:20

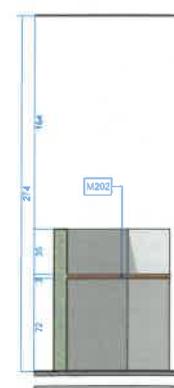


C.2 RECEPTION DESK 1:20

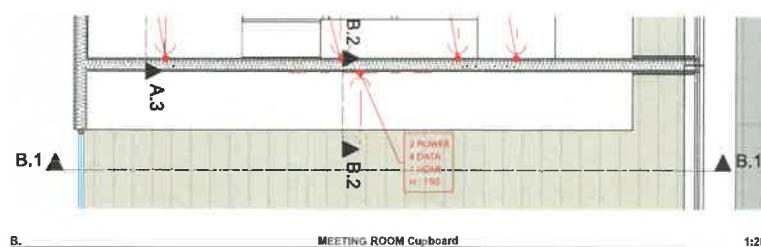


B.1 MEETING ROOM Cup-board 1:20

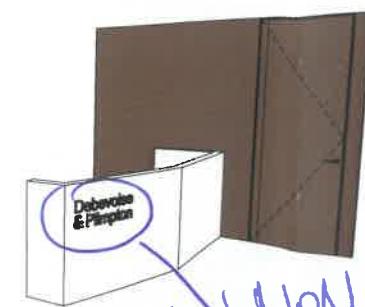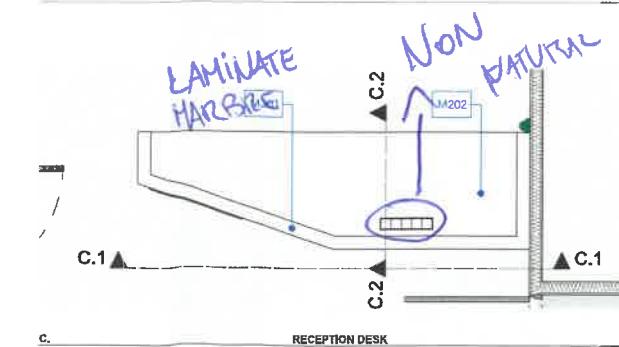


C&W DESIGN + BUILD			
CLIENT			
Debevoise & Plimpton			
PROJECT OF-ABE-21.90550 DEBEVOISE_PROJECT			
NOTE All drawings are the sole property of C&W Design + Build and may not be used without their written permission. Copying dimensions only are to be made for internal use only. Any copying and/or scaling of the drawing will be at the Supplier's risk. Suppliers are to verify all dimensions given and any discrepancy shall be addressed to the Supplier. The Supplier shall be liable for any discrepancy found. Any claims for variations or errors shall be submitted to the Client for assessment prior to agreement of any such variation or error.			
PHASE DESIGN			
DOCUMENT			
81.01 Joinery details			
APPROVALS C&W D+8			
CLIENT			
File date: 21/07/22 Scale: 1:20, 1:42.2, 1:99.57			
REVISION			
Revision	ID	Nom de changement	Date
D1			1/10/21
D2			21/10/21
D3			8/11/21
D4			25/11/21
D5			1/12/21
D6			9/12/21
D7			14/12/21
E1			21/01/22

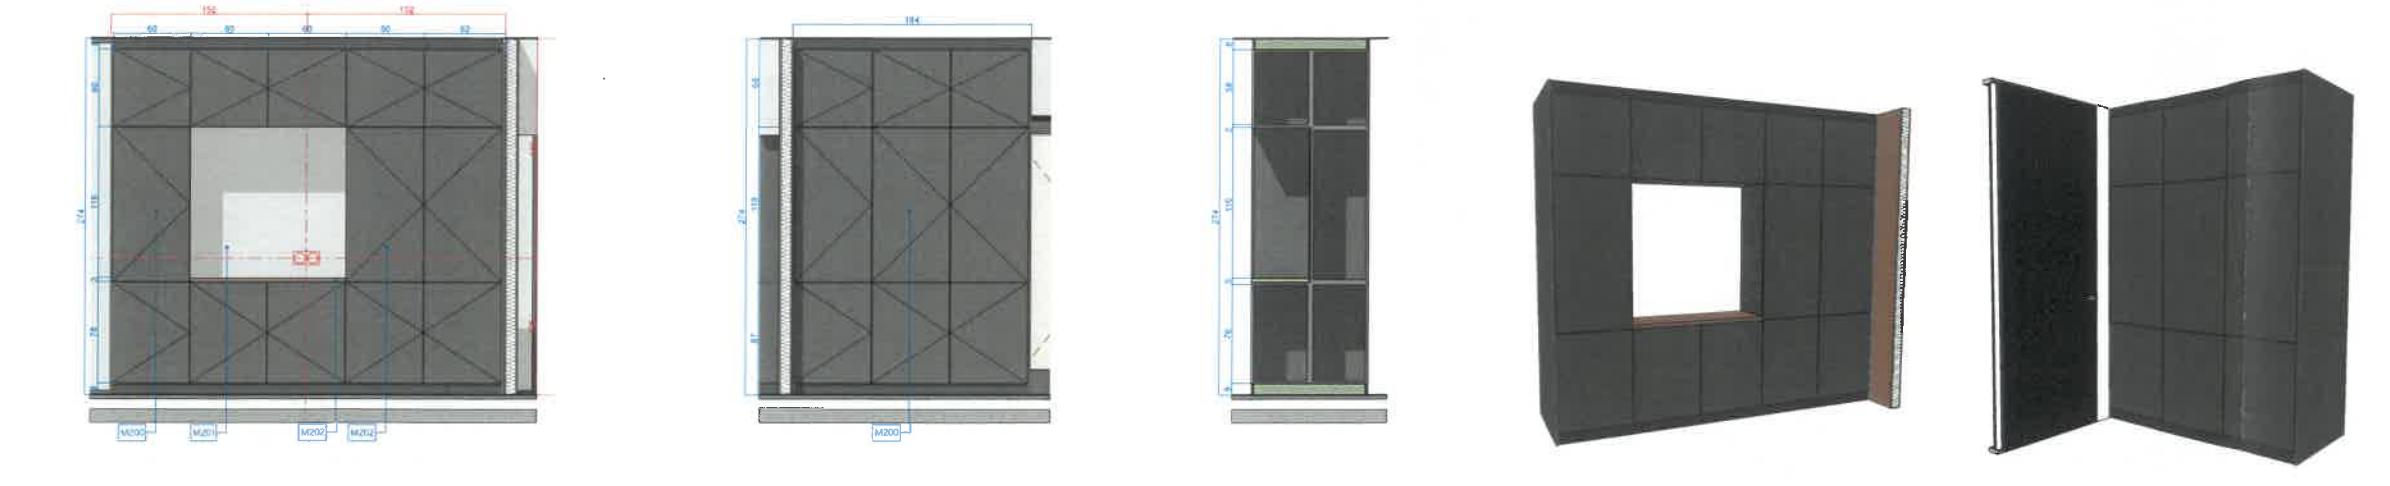


D.1 RECEPTION Cupboard 1:20 D.2 RECEPTION Cupboard 1:20 D.3 RECEPTION Cupboard 1:20 Perspective 1:103,23 RECEPTION Cupboard2 Perspective 1:101,76

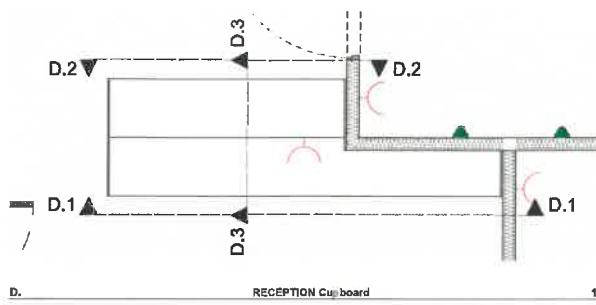


D. RECEPTION Cupboard 1:20

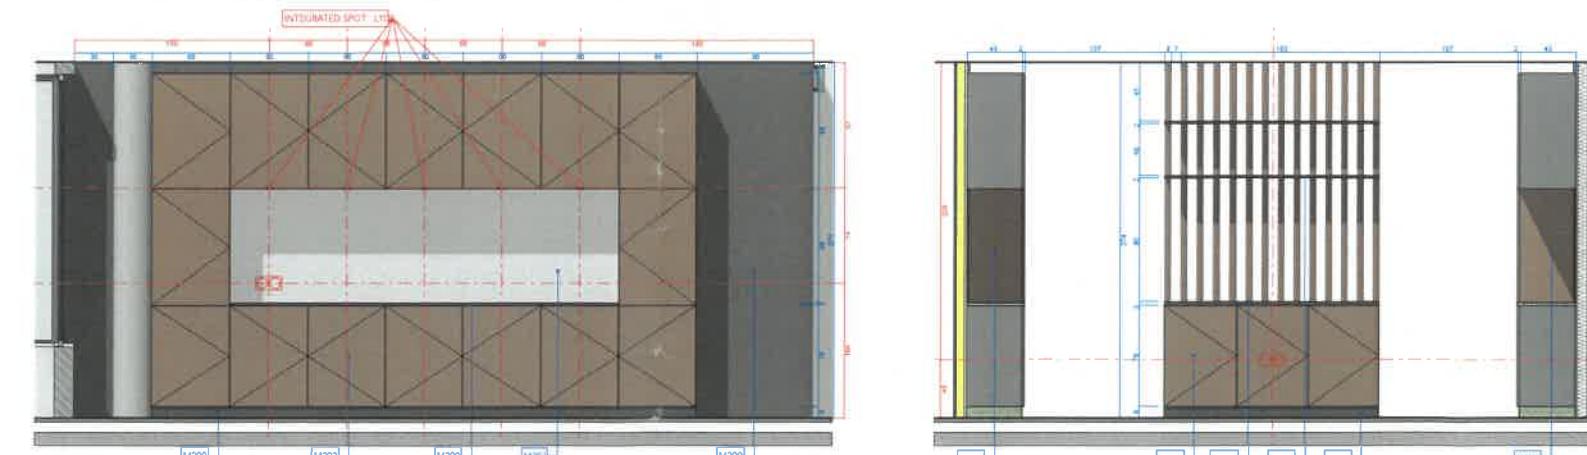


E.1 OPEN SPACE Cupboard 1:20 E.3 OPEN SPACE Cupboard 1:20

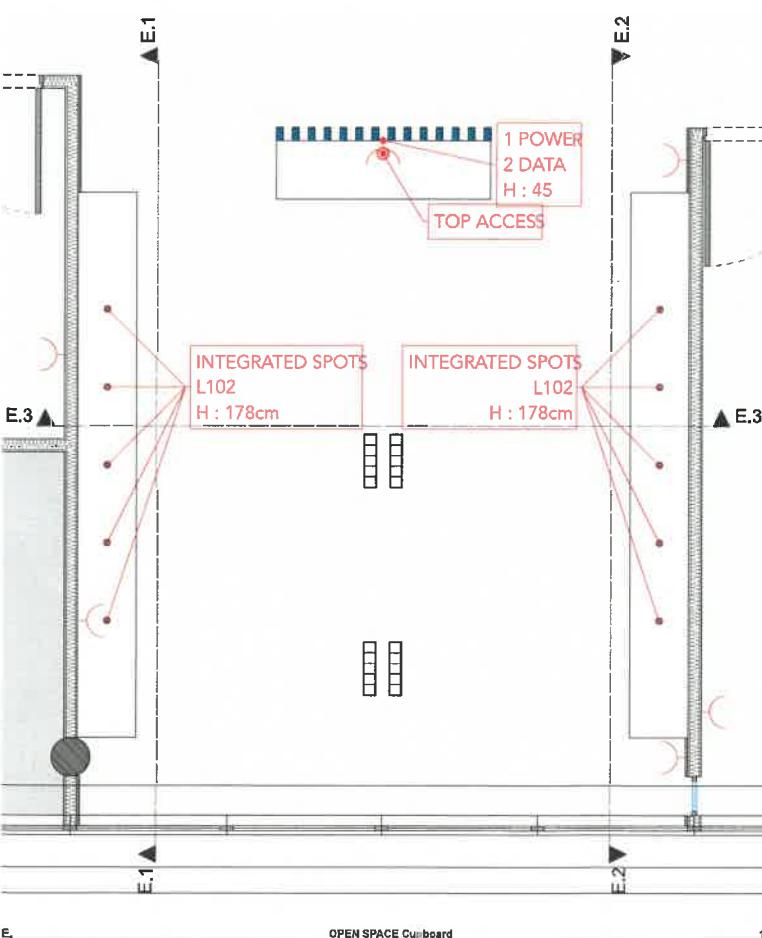


E. OPEN SPACE Cupboard 1:20

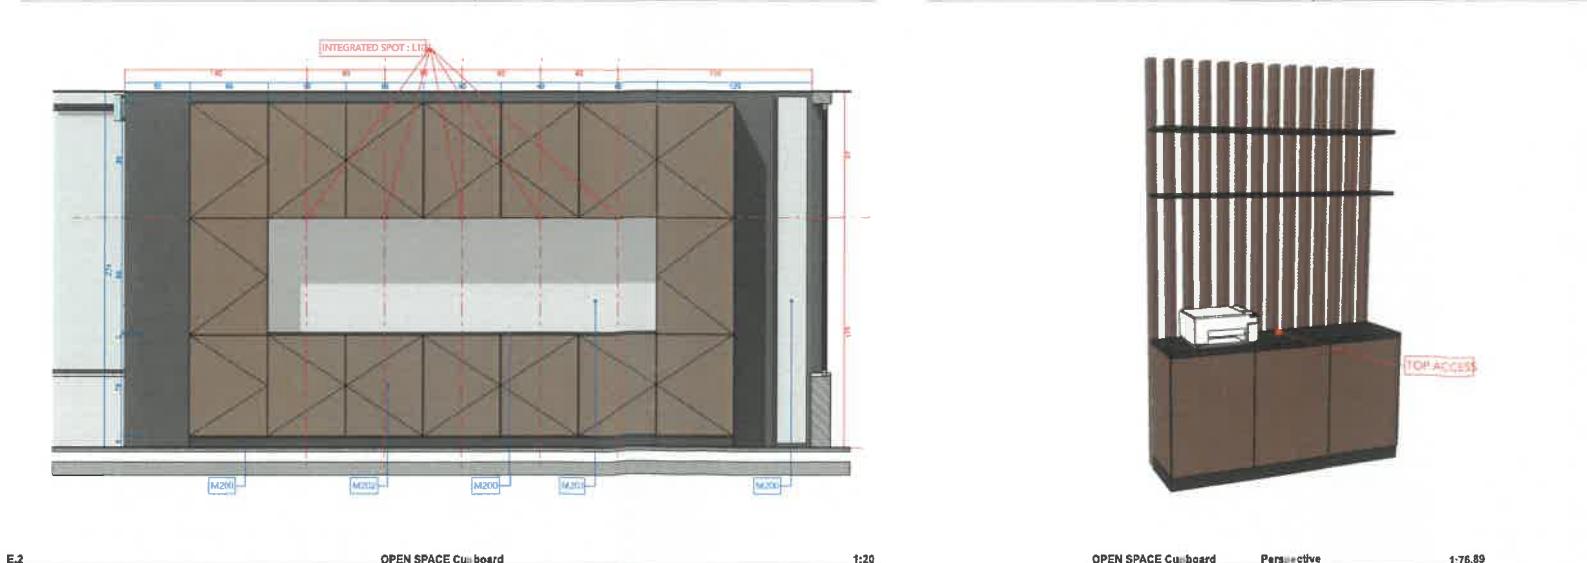


E.1 OPEN SPACE Cupboard 1:20 E.2 OPEN SPACE Cupboard 1:20 OPEN SPACE Cupboard Perspective 1:76,89

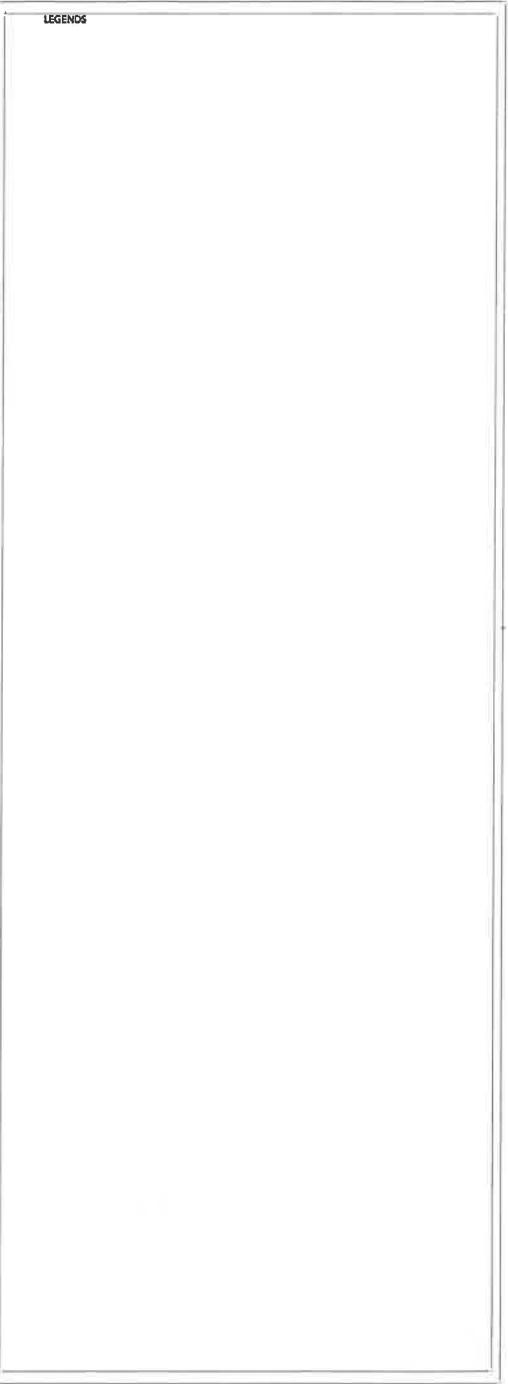


C&W DESIGN + BUILD		
CLIENT		
Debevoise & Plimpton		
PROJECT OF-ABE-21-90550 DEBEVOISE_PROJECT		
NOTE All designs are the sole property of C&W Design + Build and may not be used without their written permission. Technical drawings only are to be submitted to the Supplier and any drawing of the design or any part thereof in the possession of the Supplier, Sub-contractors and any subcontractor shall be destroyed in writing to the Supplier prior to the start of the project. Otherwise, the Supplier shall bear full responsibility for the intellectual property rights of the design.		
PHASE DESIGN		
DOCUMENT 81.02 Joinery details		
APPROVALS	C&W D&B	CLIENT
Print date : 21/07/22 Scale : 1:20, 1:76,89, 1:103,23, 1:101,76		
REVISION		
Revision	ID	Nom de changement
D1		Date 19/10/21
D2		21/10/21
D3		8/11/21
D4		25/11/21
D5		1/12/21
D6		9/12/21
D7		14/12/21
E1		21/01/22
DOCUMENT 81.02		
REASON E1		

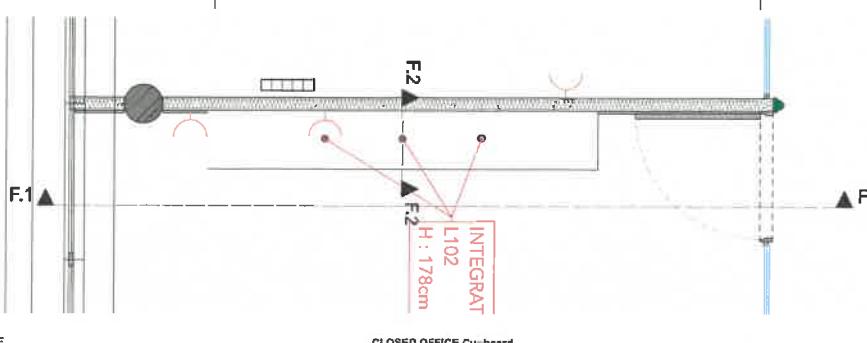


F.1 CLOSED OFFICE Cupboard 1:20

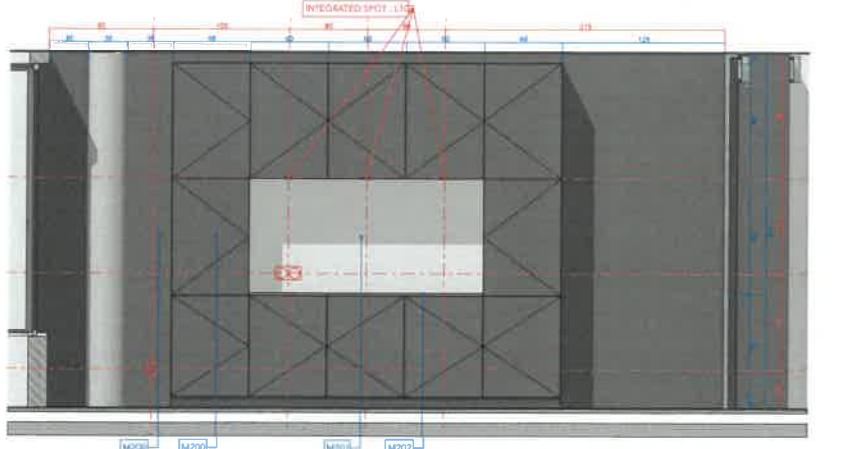


F.1 CLOSED OFFICE Cupboard 1:20 F.2 CLOSED OFFICE Cupboard 1:20

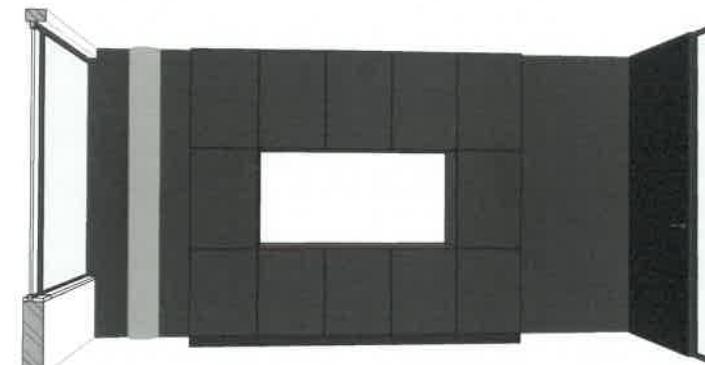


CLOSED OFFICE Cupboard Perspective 1:97.83

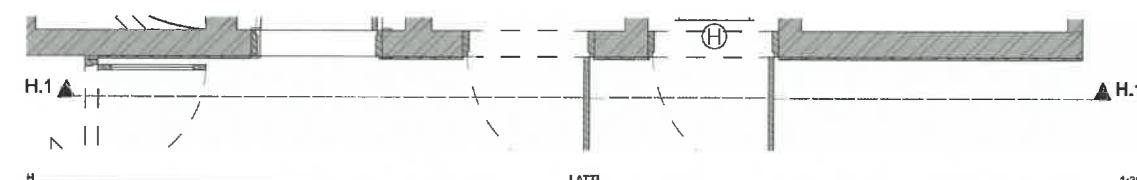

H.1 LATI 1:20

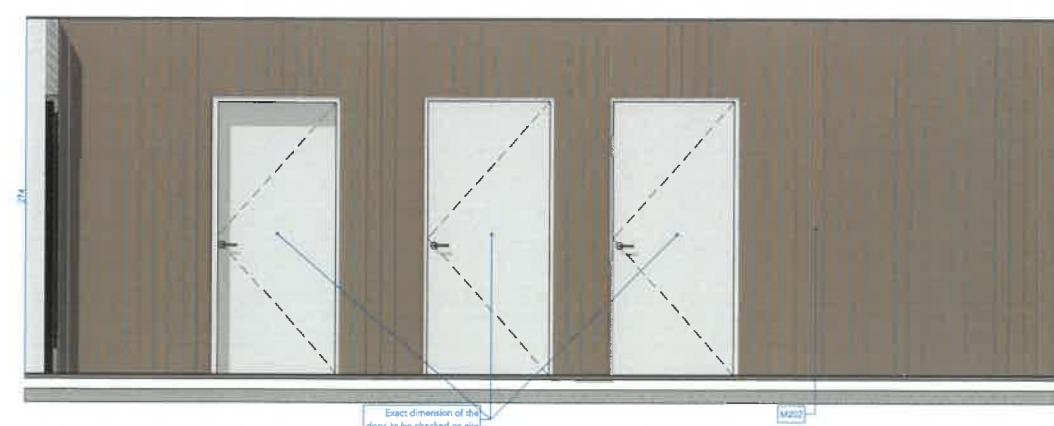


H.1 Latti 1:20

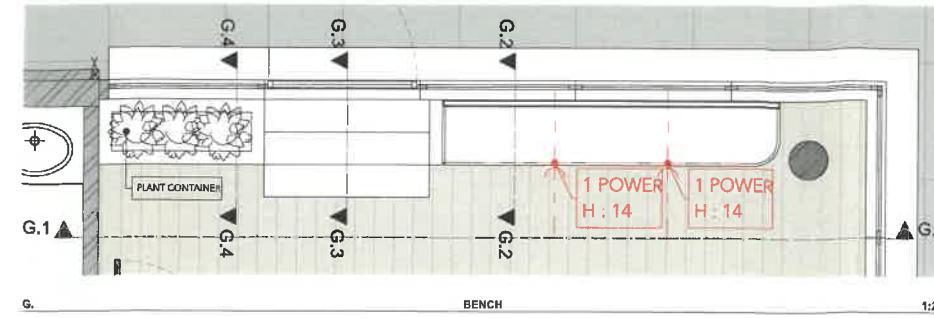

G.1 G.2 G.3 G.4 BENCH 1:20




G.1 BENCH 1:20

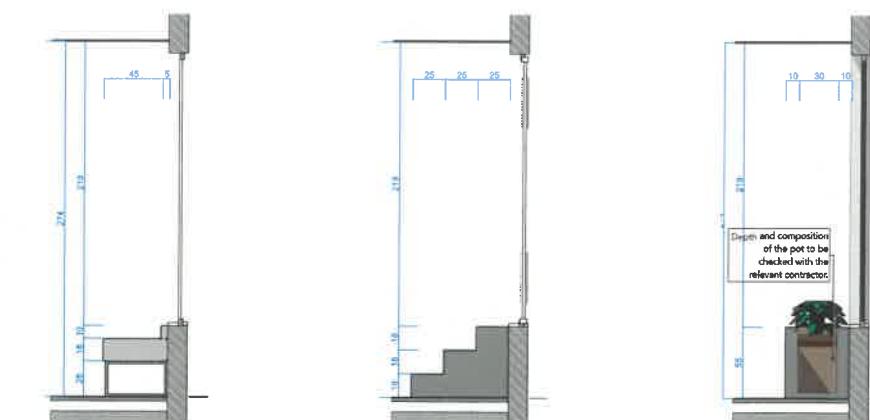

G.2 BENCH 1:20 G.3 BENCH 1:20 G.4 BENCH 1:20



BENCH Perspective 1:97.56

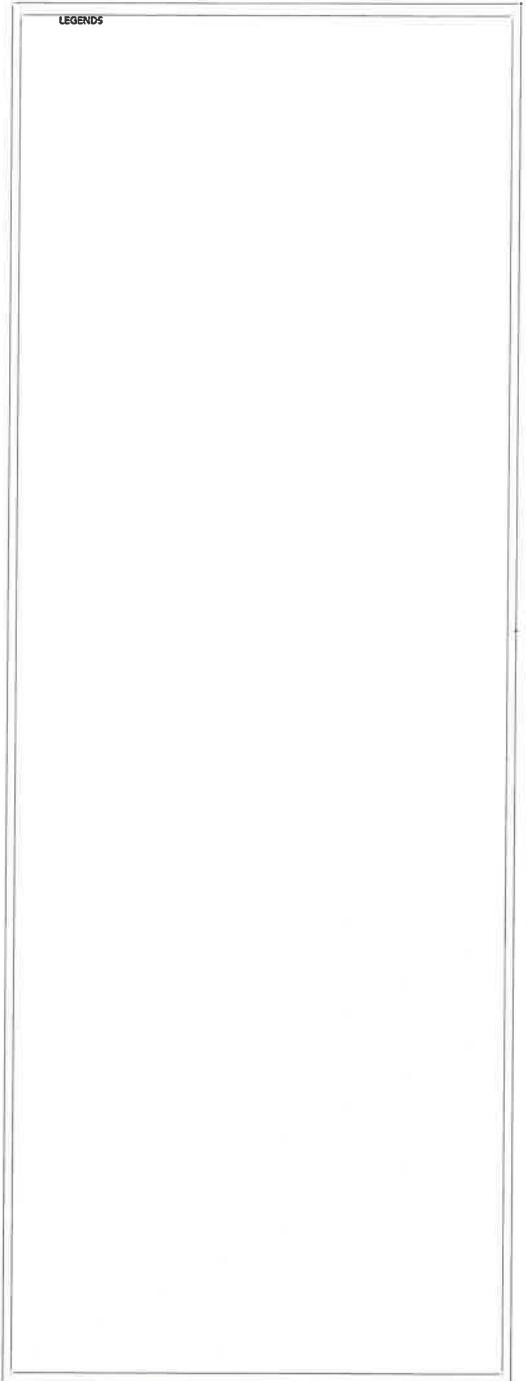

C&W DESIGN + BUILD

Debevoise & Plimpton

**OF-ABE-21.9050
DEBEVOISE_PROJECT**

NOTE

All designs are the sole property of Cuthbertson/Hirstfield Design + Build and may not be used without their written permission. Any dimensions only are to be added to the drawings by the contractor and any alterations will be at the Supplier's risk. Suppliers are to verify all dimensions given and any discrepancies shall be notified to the contractor. The contractor shall be responsible for any errors or omissions in the drawings and shall be liable for any damage caused by any such omission or error.

PHASE

DESIGN

DOCUMENT

**81.03
Joinery details**

APPROVALS

C&W D+B

CLIENT

REVISION

Revision ID Nom de changement Date

D1 19/10/21

D2 21/10/21

D3 01/11/21

D4 25/11/21

D5 1/12/21

D6 9/12/21

D7 14/12/21

E1 21/01/22

**Print date: 21/01/22
Scale: 1:20, L14, R2, T97.56**

DOCUMENT N°

81.03

REVISION

E1

Page: 10/24