




Coupe 1

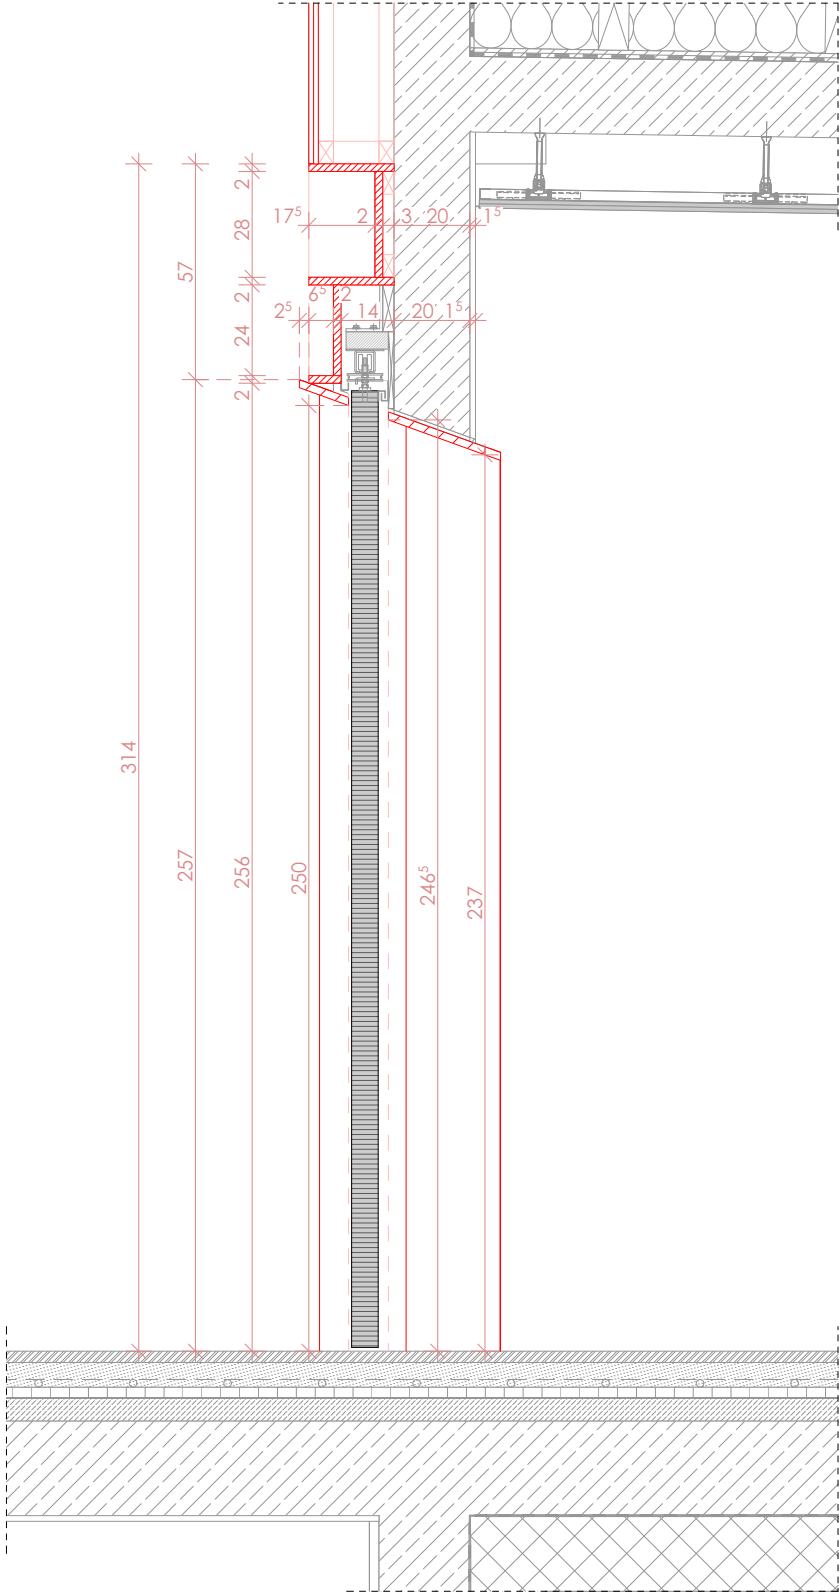

Coupe 2

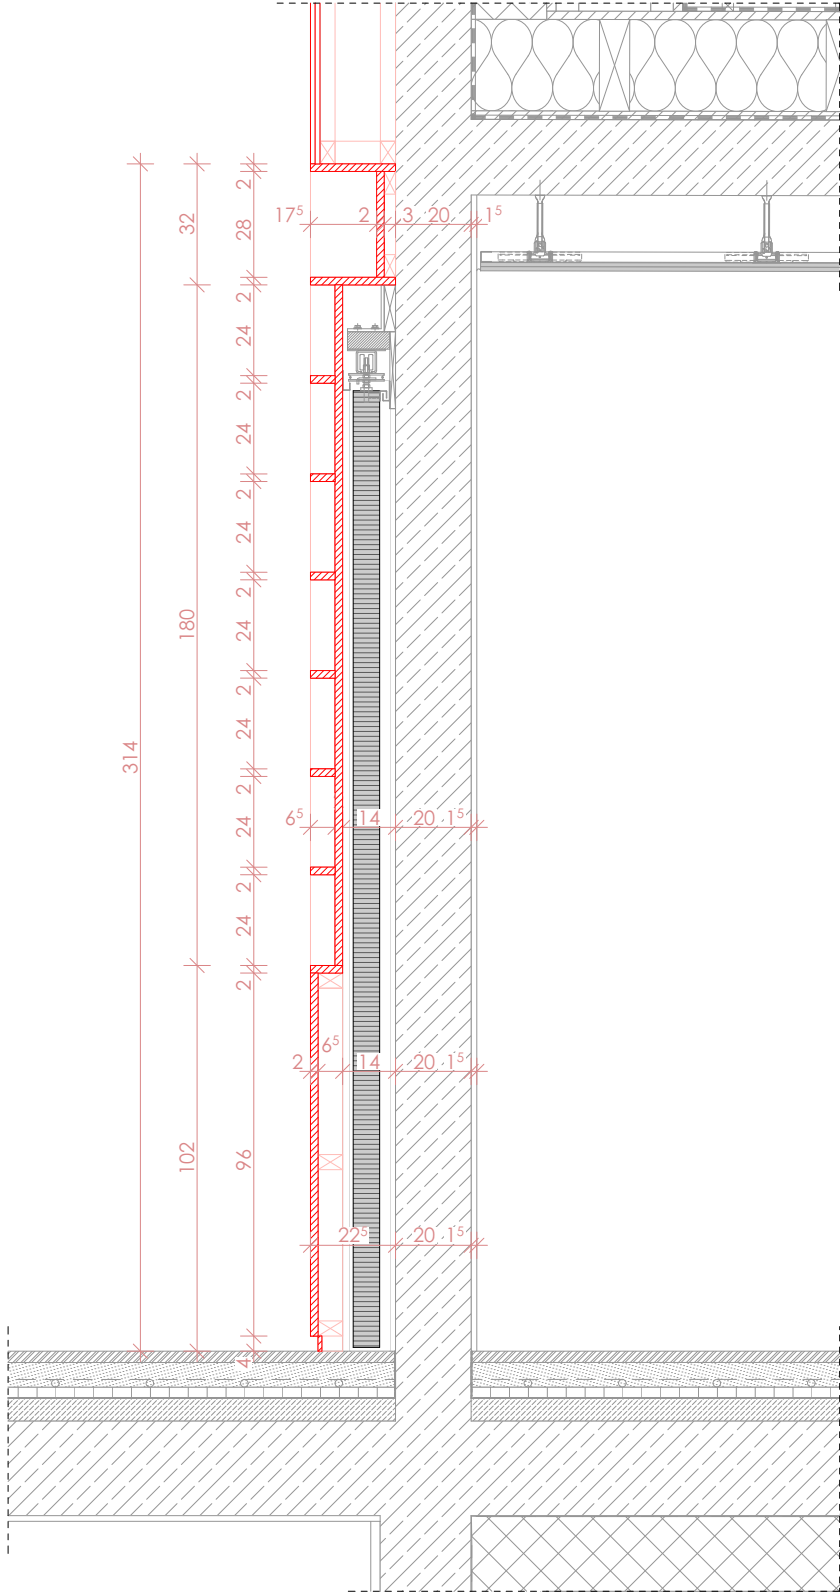

Coupe 3

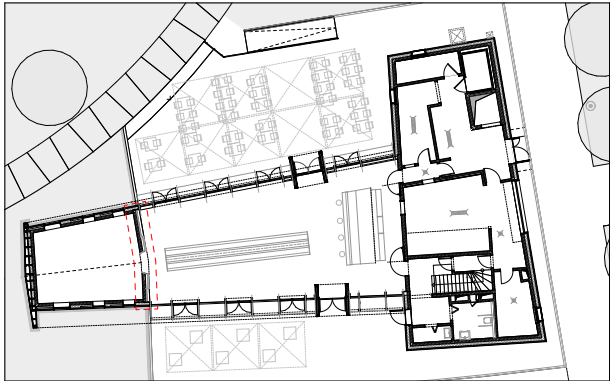

1803	Brasserie Parc Gasperich	Boulevard de Kockelscheur Luxembourg ville
Numéro projet	Projet	
Maître d'ouvrage	VILLE DE LUXEMBOURG	Ville de Luxembourg
Architecte	DIANE HEIREND ARCHITECTURE & URBANISME	5, rue de la Gare L-3322 Bivange tél: (+352) 485787-1 e-mail: info@dianeheirend.com

DETAIL 12.2 - Étagère murale salle				1:20	A3	EB	28.08.2023
Contenu	Echelle	Format	Dessiné par	Date			
AR	EXE	DET		50.5.12.2	N00		
Émetteur	Phase	Not	Zone	Numéro	Niv	Indice	